



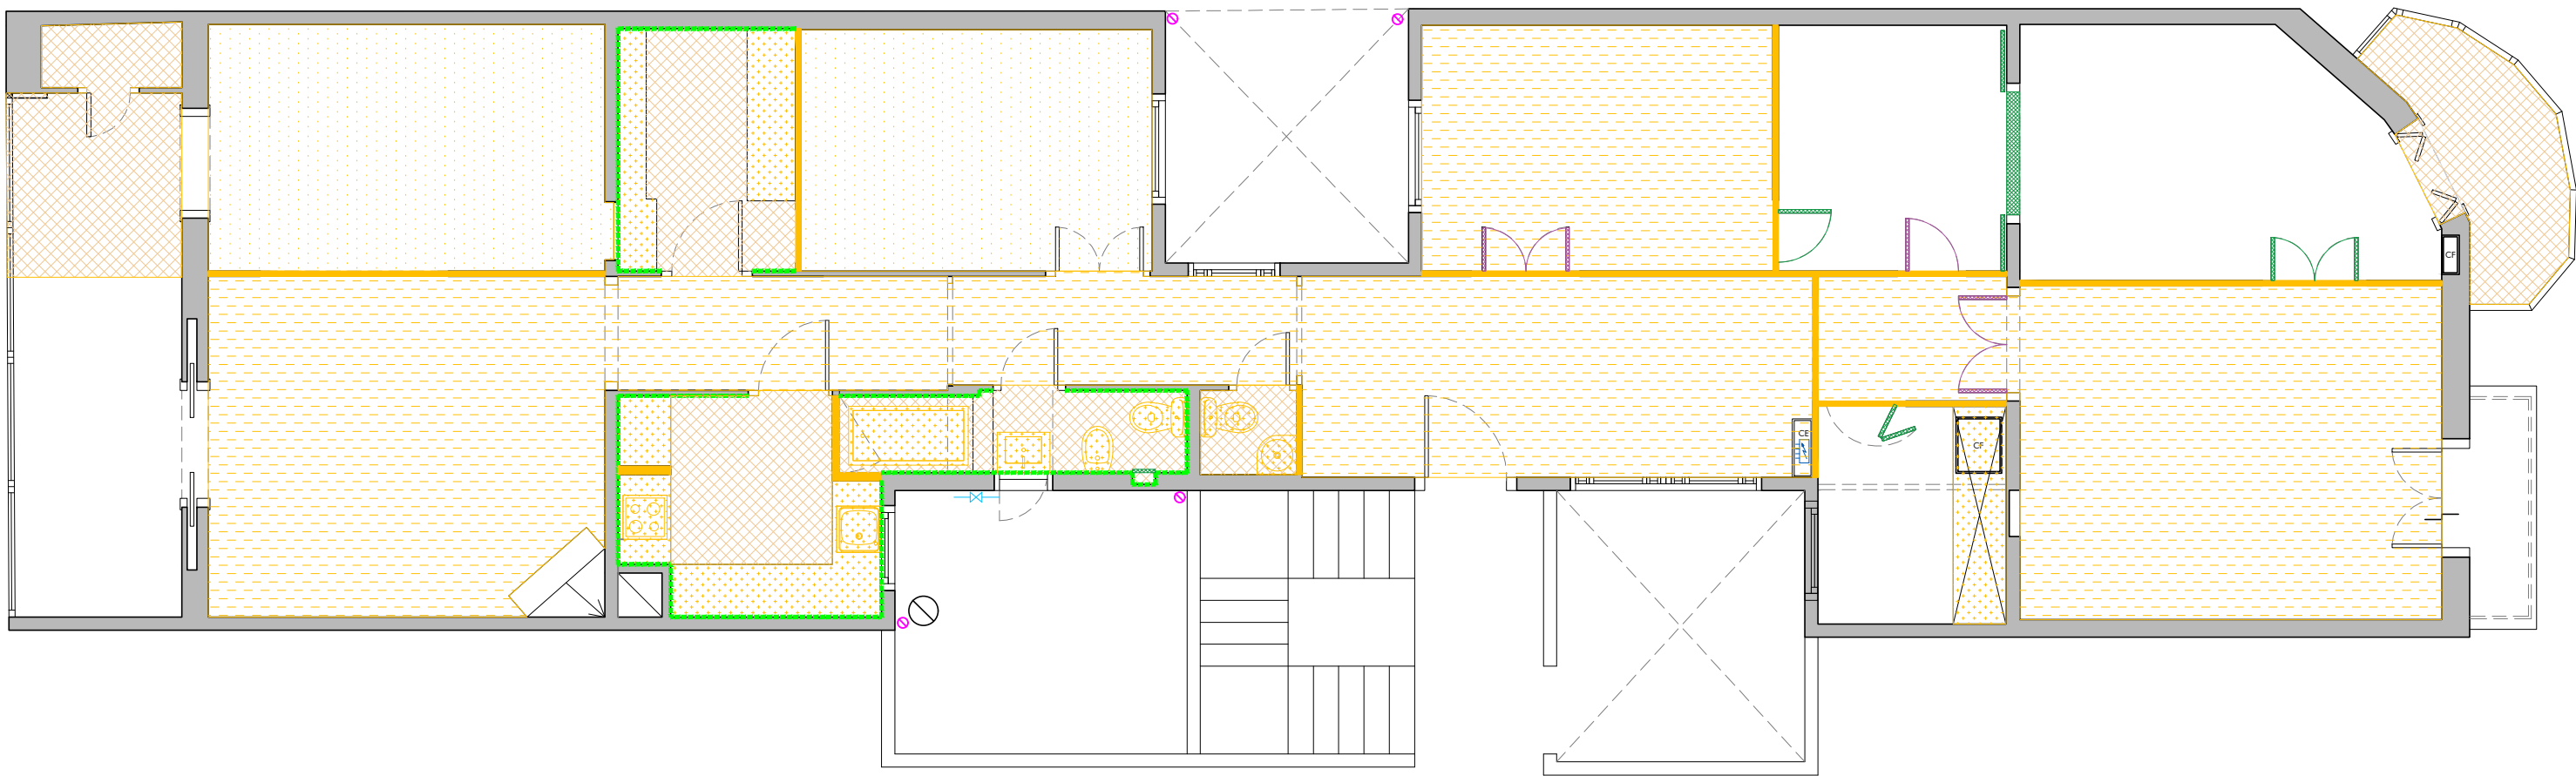

- | | | | |
|--|---|---|---|
|  | DERRIBO MUROS |  | DERRIBO REVESTIMIENTOS PARED |
|  | DERRIBO DE ELEMENTOS FIJOS
(MOBILIARIO FIJO, SANITARIOS, etc...) |  | RETIRAR PARQUET |
|  | RETIRAR MOQUETA |  | RETIRAR Y CONSERVAR CARPINTERIA/PUERTAS |
|  | DERRIBO PAVIMENTOS |  | RETIRAR CARPINTERIA/PUERTAS |

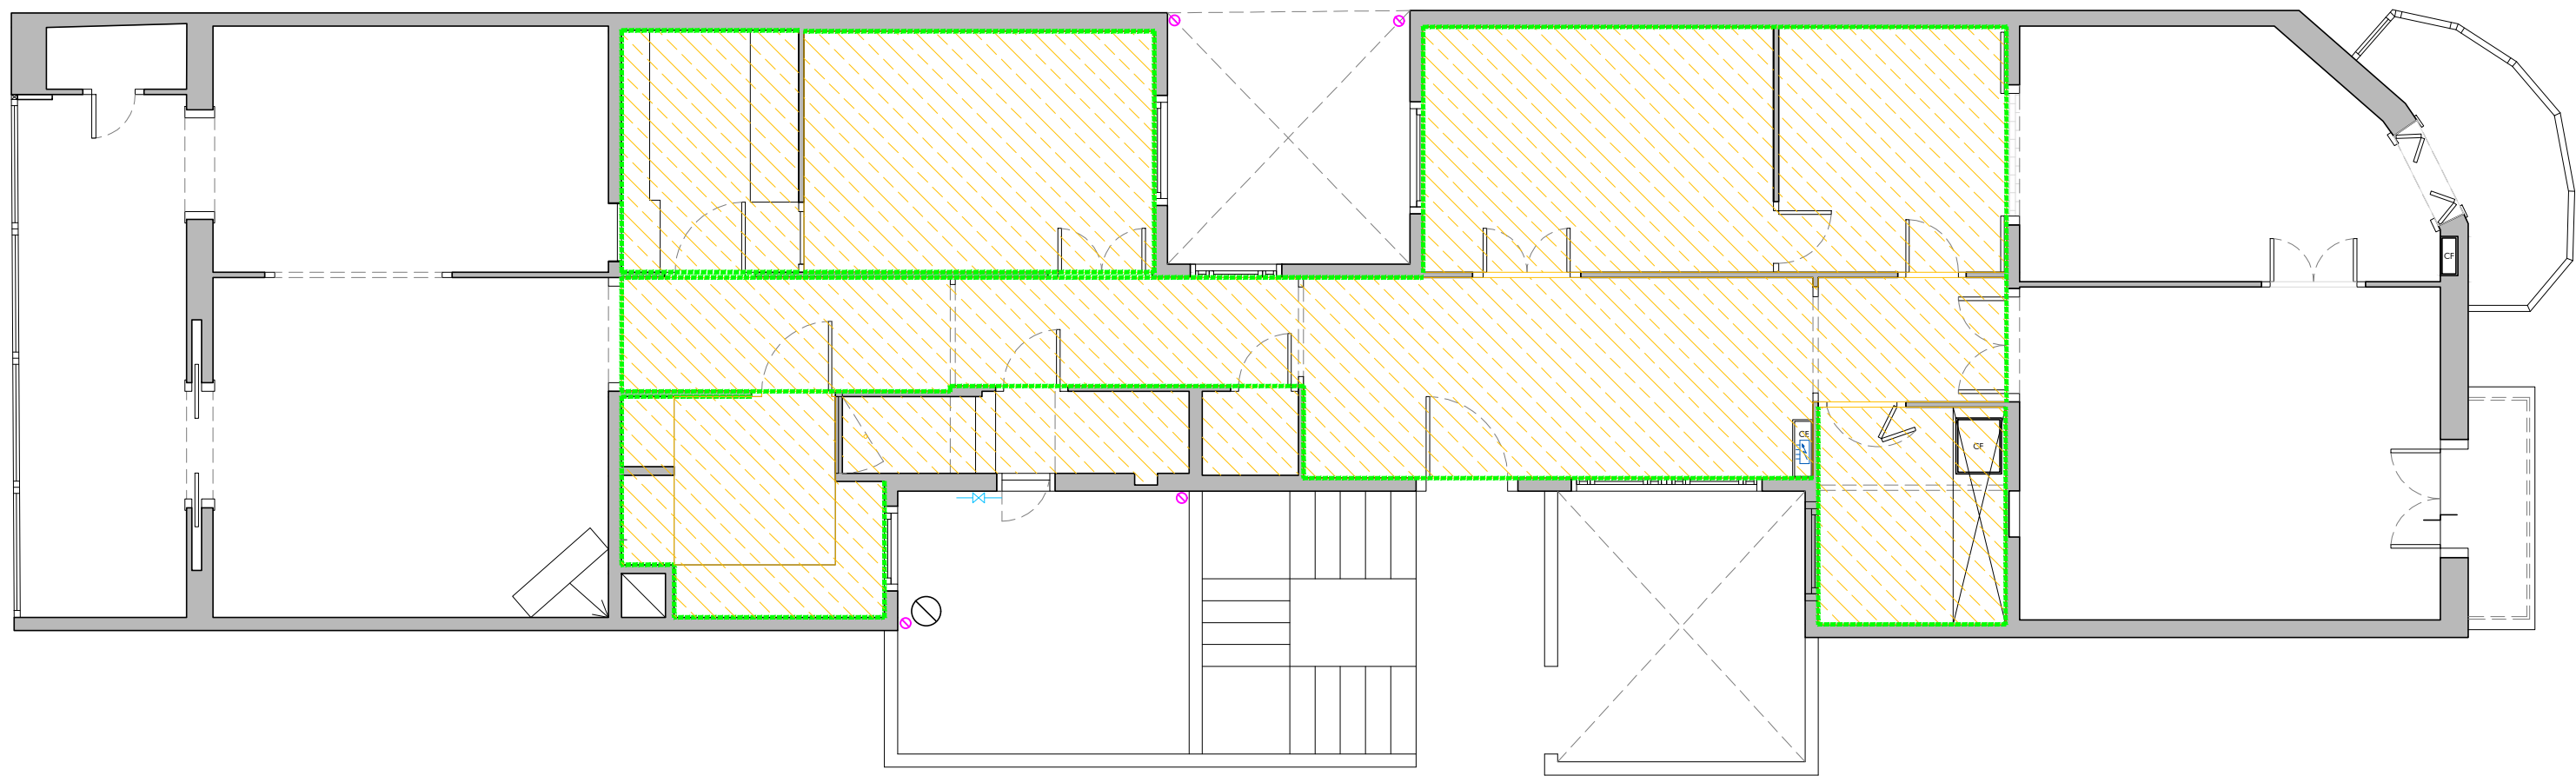

 DERRIBO FALSO TECHO

 DERRIBO CORNISAS

